


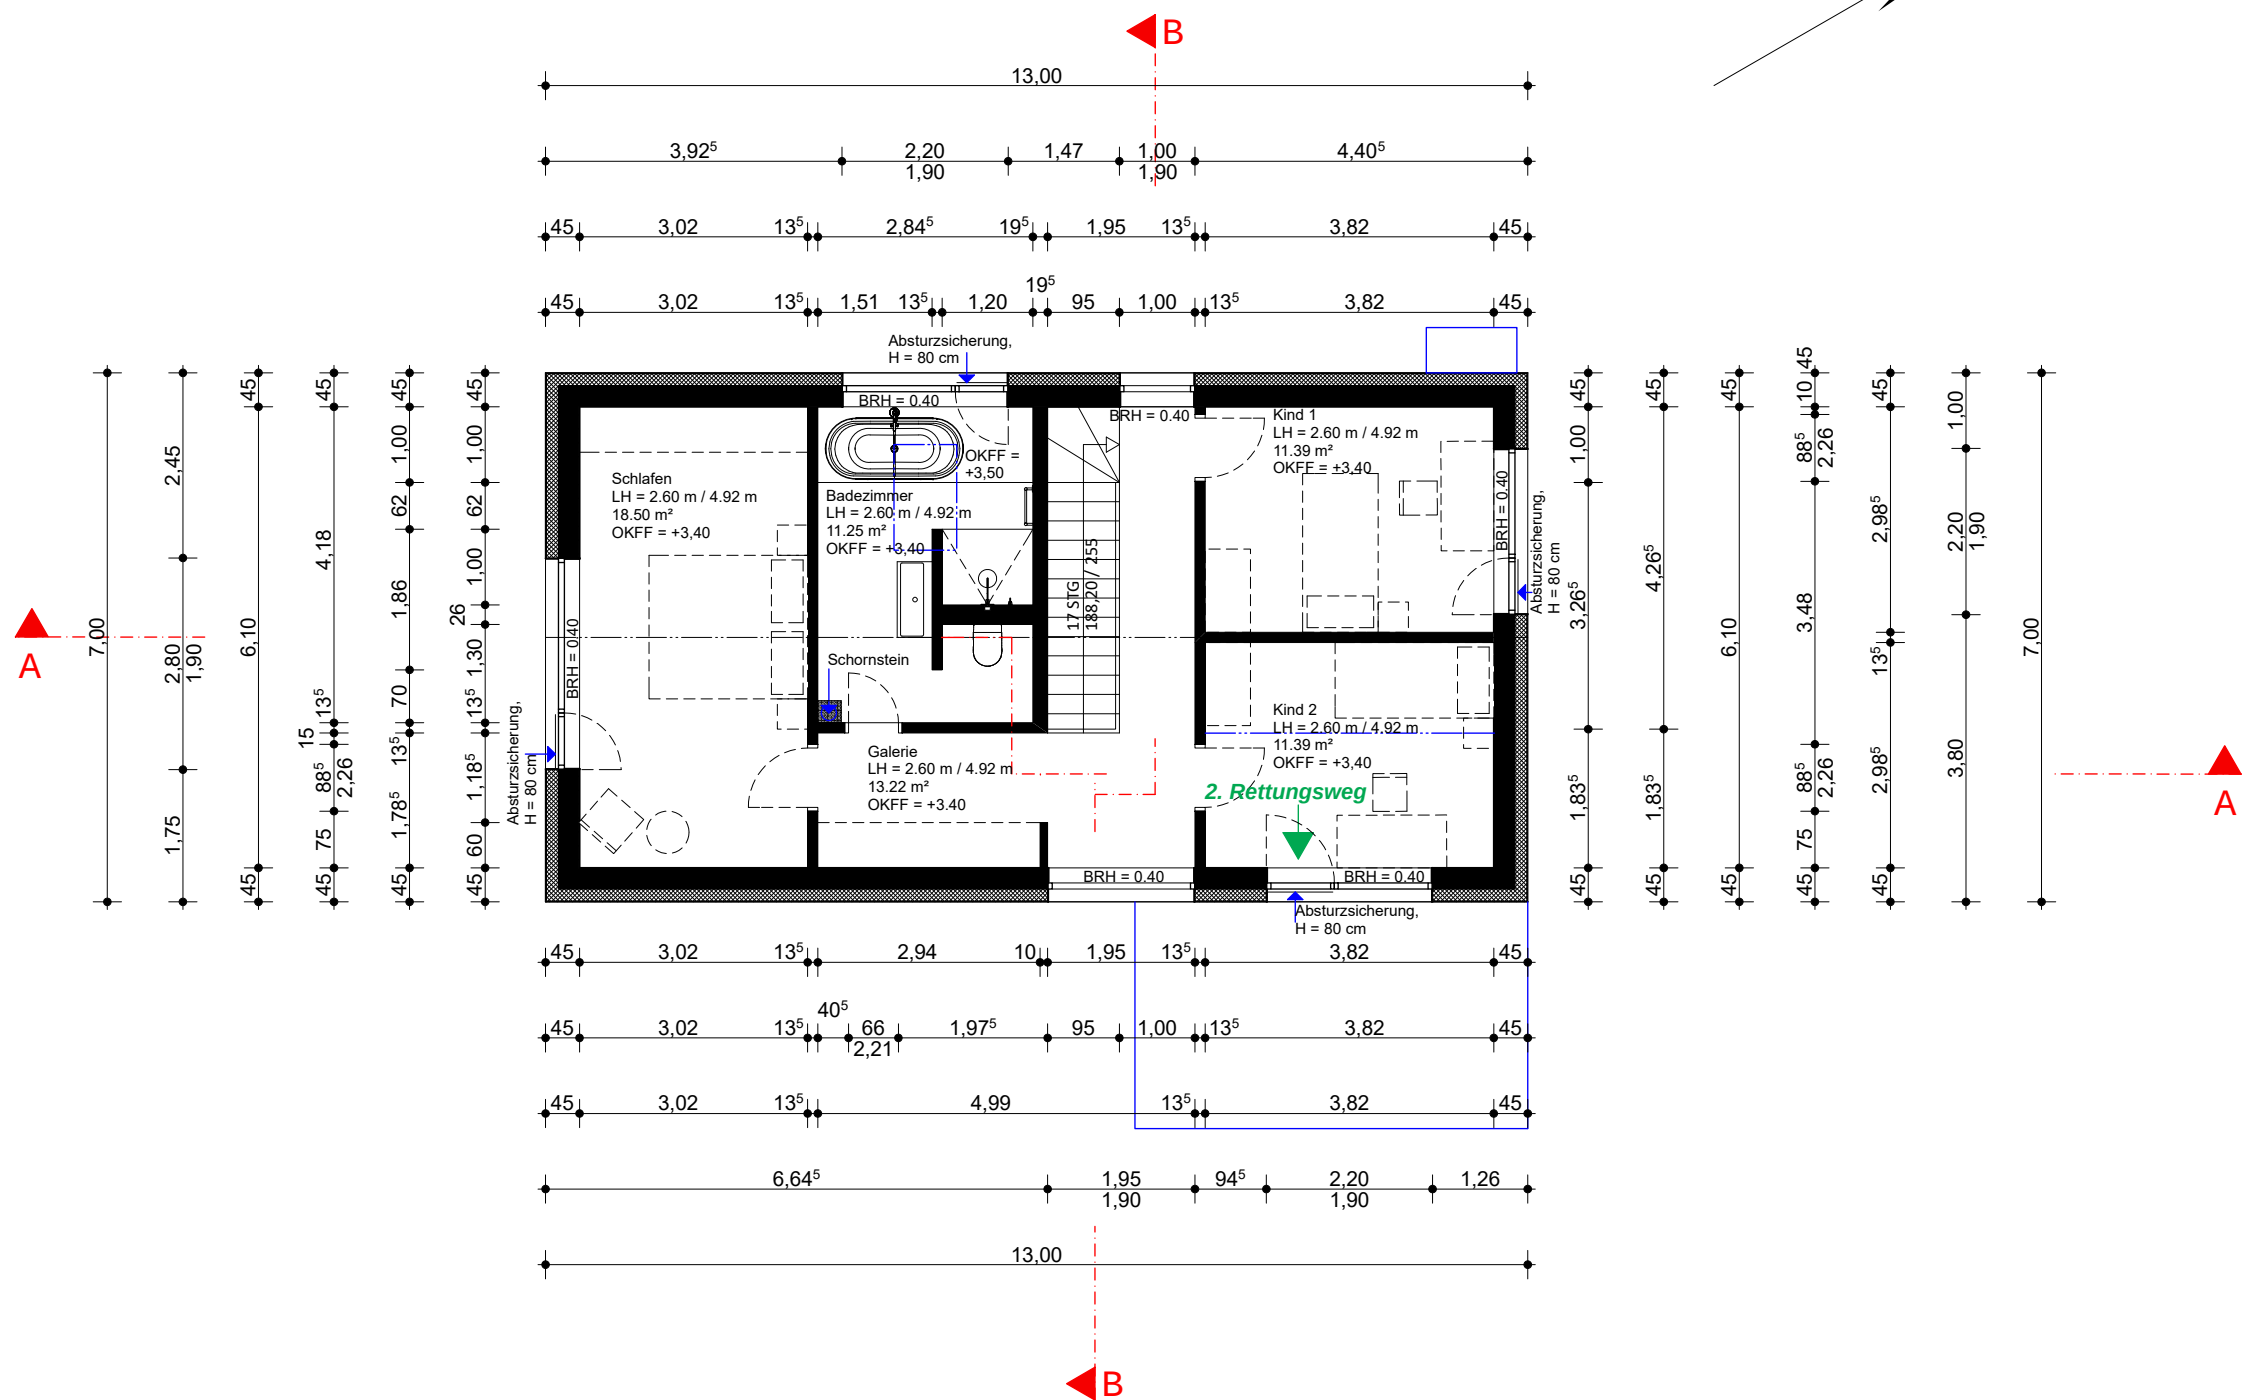

OK FFB EG = +/- 0.00 = + 44.20 ü. NHN
OK RFB EG = - 0.20 = + 44.00 ü. NHN

0 m 1 m 5 m

BAUVORHABEN:
Neubau eines Einfamilienhauses
Mittelsteg 46 B
13158 Berlin

AUFTRAGGEBER:
Katharina und Dr. Alexander Berlin
Fontanestraße 54
13158 Berlin
Tel: 0173 2067659
E-Mail: berlin.alexander@icloud.com

ARCHITEKT:
Ing. arch. Valerie Söder
Rykestraße 3
10405 Berlin
Tel: 015752611190, 030 609 828 521
Fax: 030 609 828 529
E-Mail: valerie@soederarchitect.com
Web: www.soederarchitect.com

02

Grundriss Obergeschoss

Genehmigungsplanung			
Maßstab	Blattgröße	Datum	Planersteller
1:100	420*297 A3	22.03. 2024	Valerie Söder